
スリーブ表 1階

干渉スリーブ　作成日: 2026年11月12日

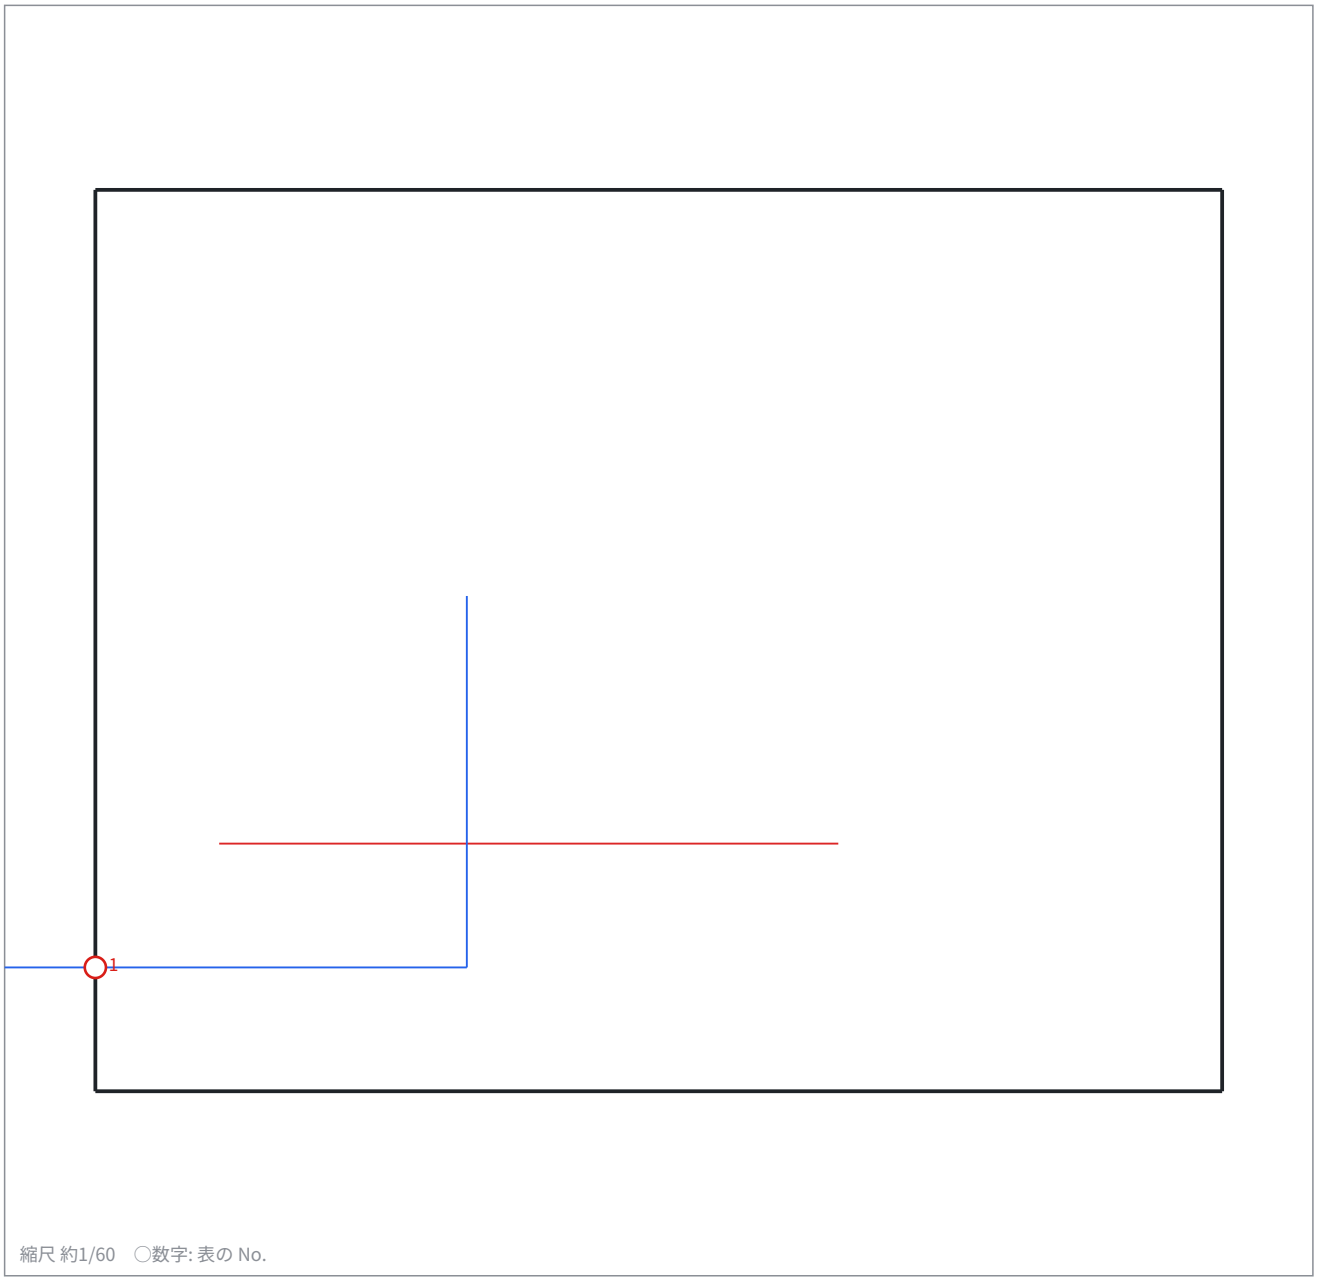


No	部位	管	スリーブ	高さ	位置 X,Y(m)
1	基礎（外周）	給水 HIVPφ20	φ65	FL-250	0.00, 1.00

スリーブ径は一般値（内径 〓 管の外径＋30mm、給湯は保温材の分＋20mm）。構造の確認をしてください
位置 X,Y は建物の左下の角から右へ・上へ（m）。配管データの座標からなので、現場で寸法を確かめてから墨出ししてください

スリーブ表 2階

干渉スリーブ　作成日: 2026年11月12日

 

縮尺 約1/60　○数字: 表の No.

No	部位	管	スリーブ	高さ	位置 X,Y(m)
2	床	給水 HIVPφ20	φ65	FL-100	5.00, 5.00

スリーブ径は一般値（内径 〓 管の外径＋30mm、給湯は保温材の分＋20mm）。構造の確認をしてください
位置 X,Y は建物の左下の角から右へ・上へ（m）。配管データの座標からなので、現場で寸法を確かめてから墨出ししてください